



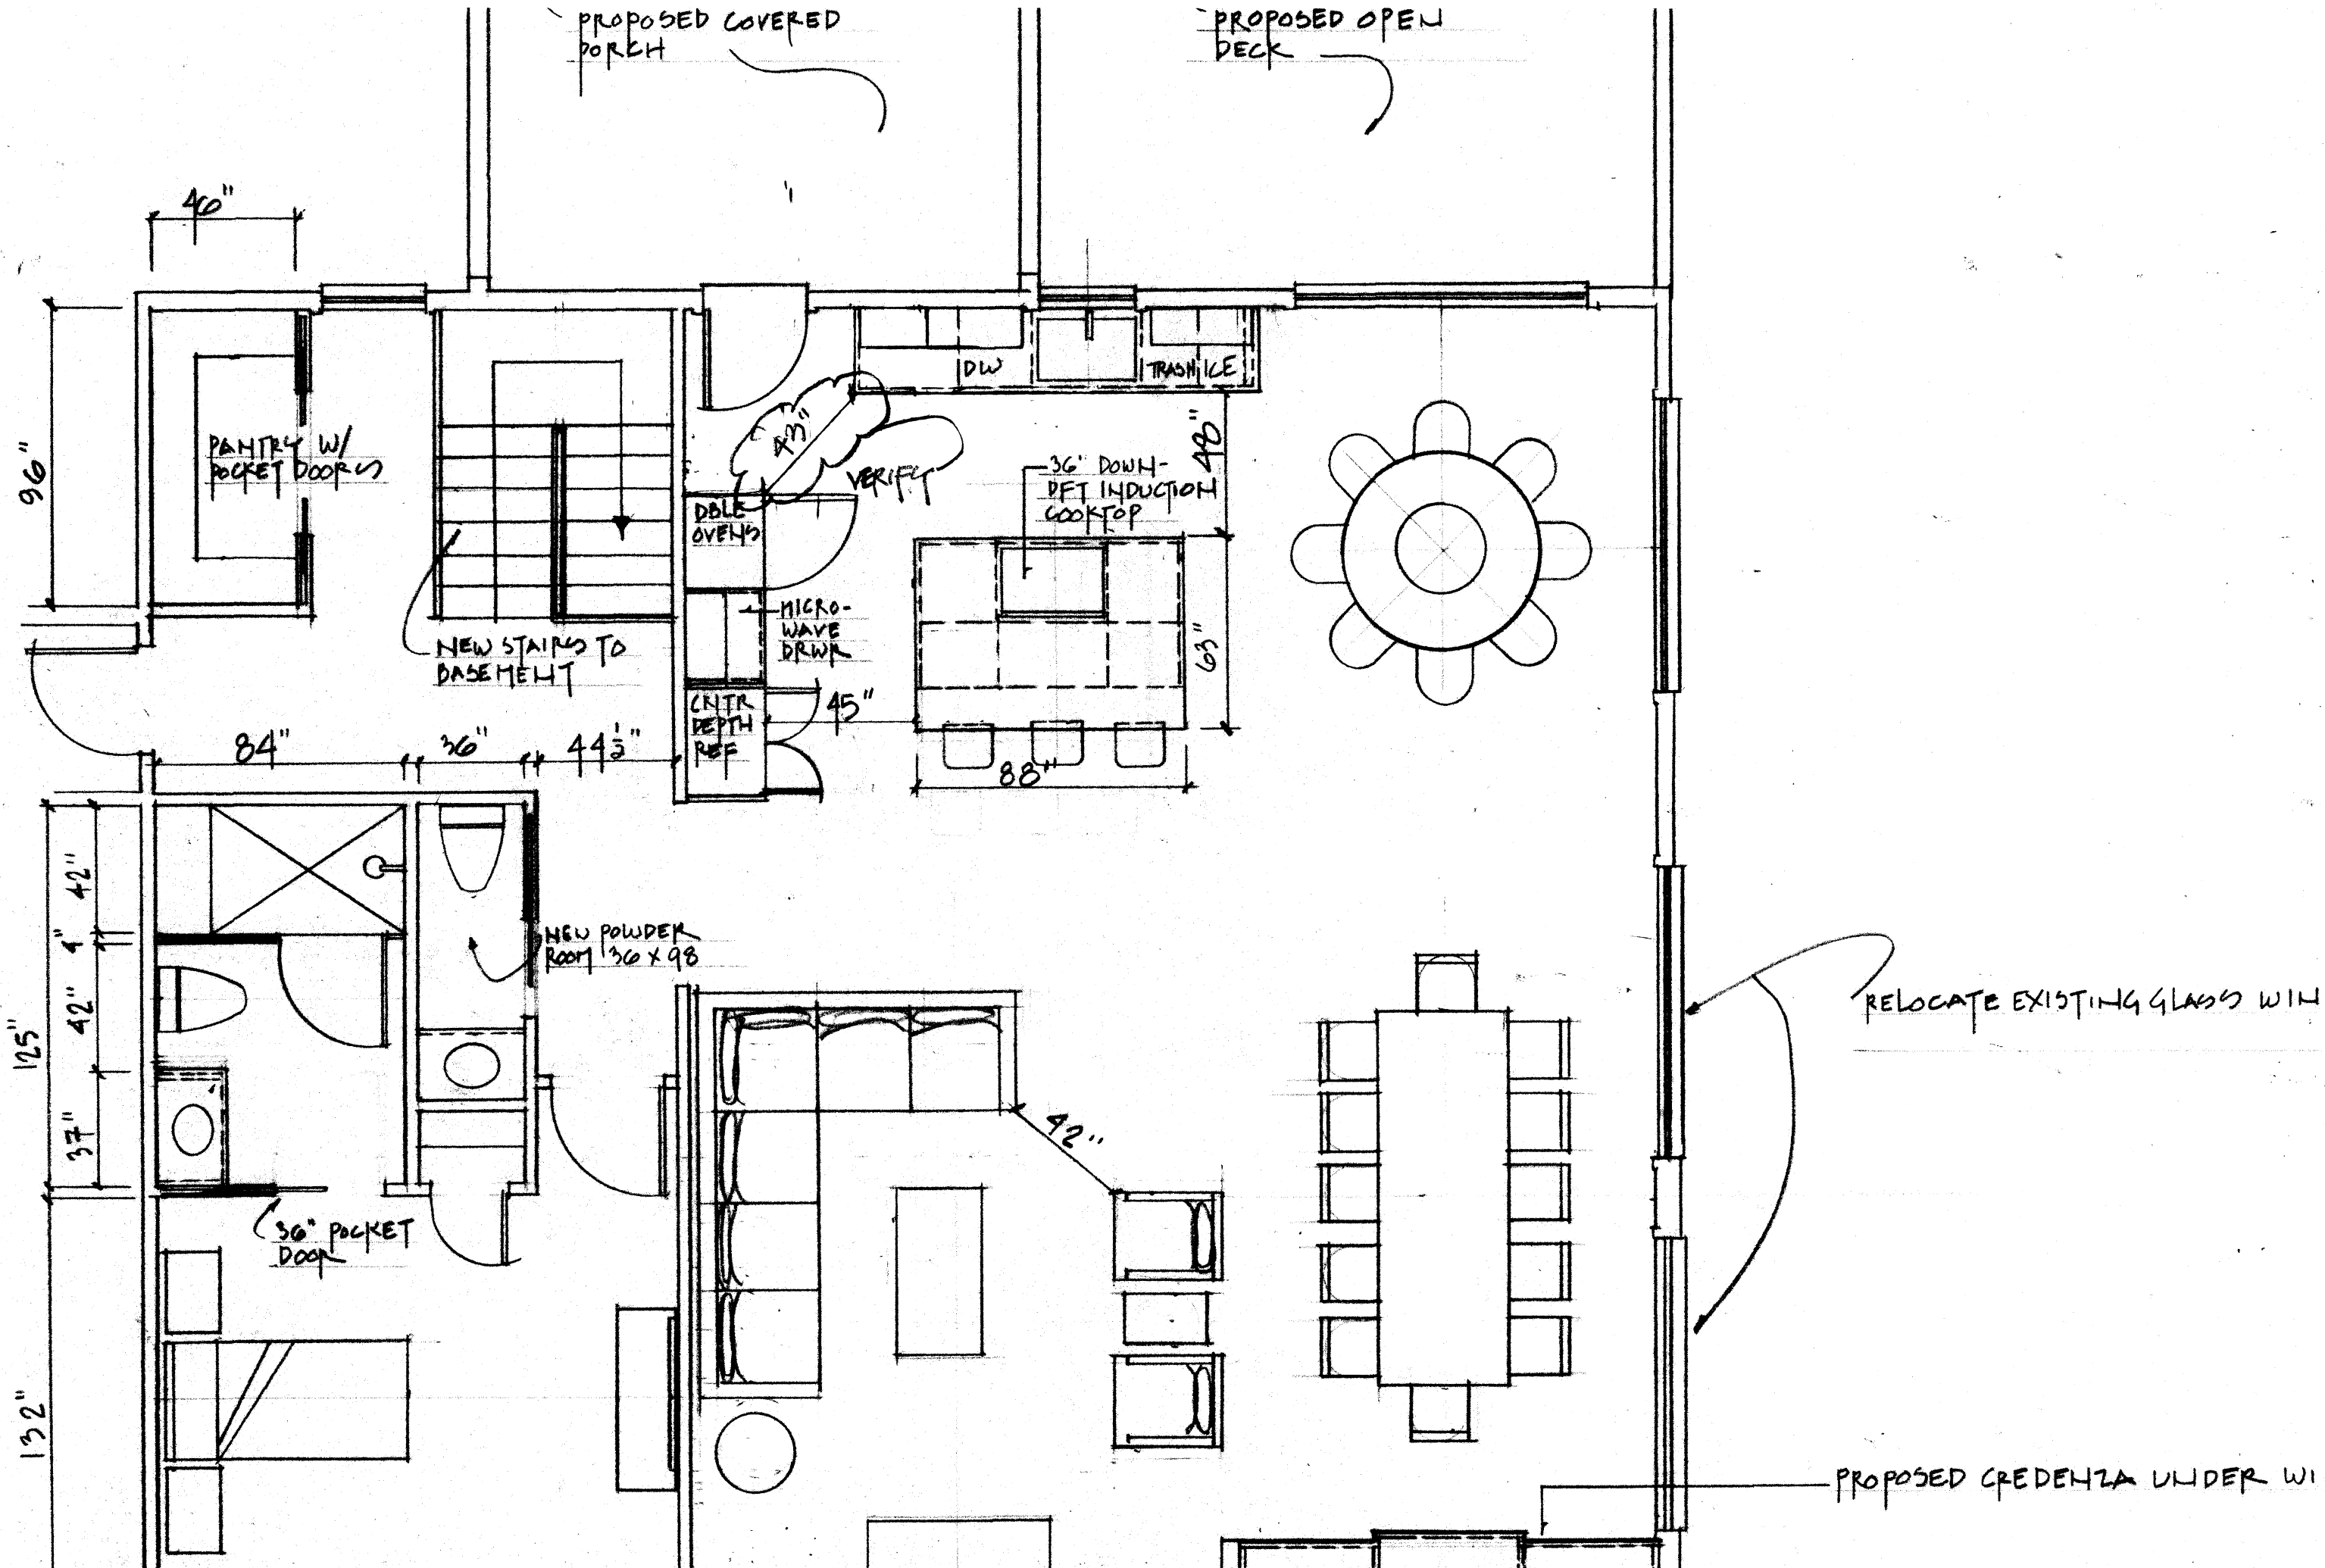

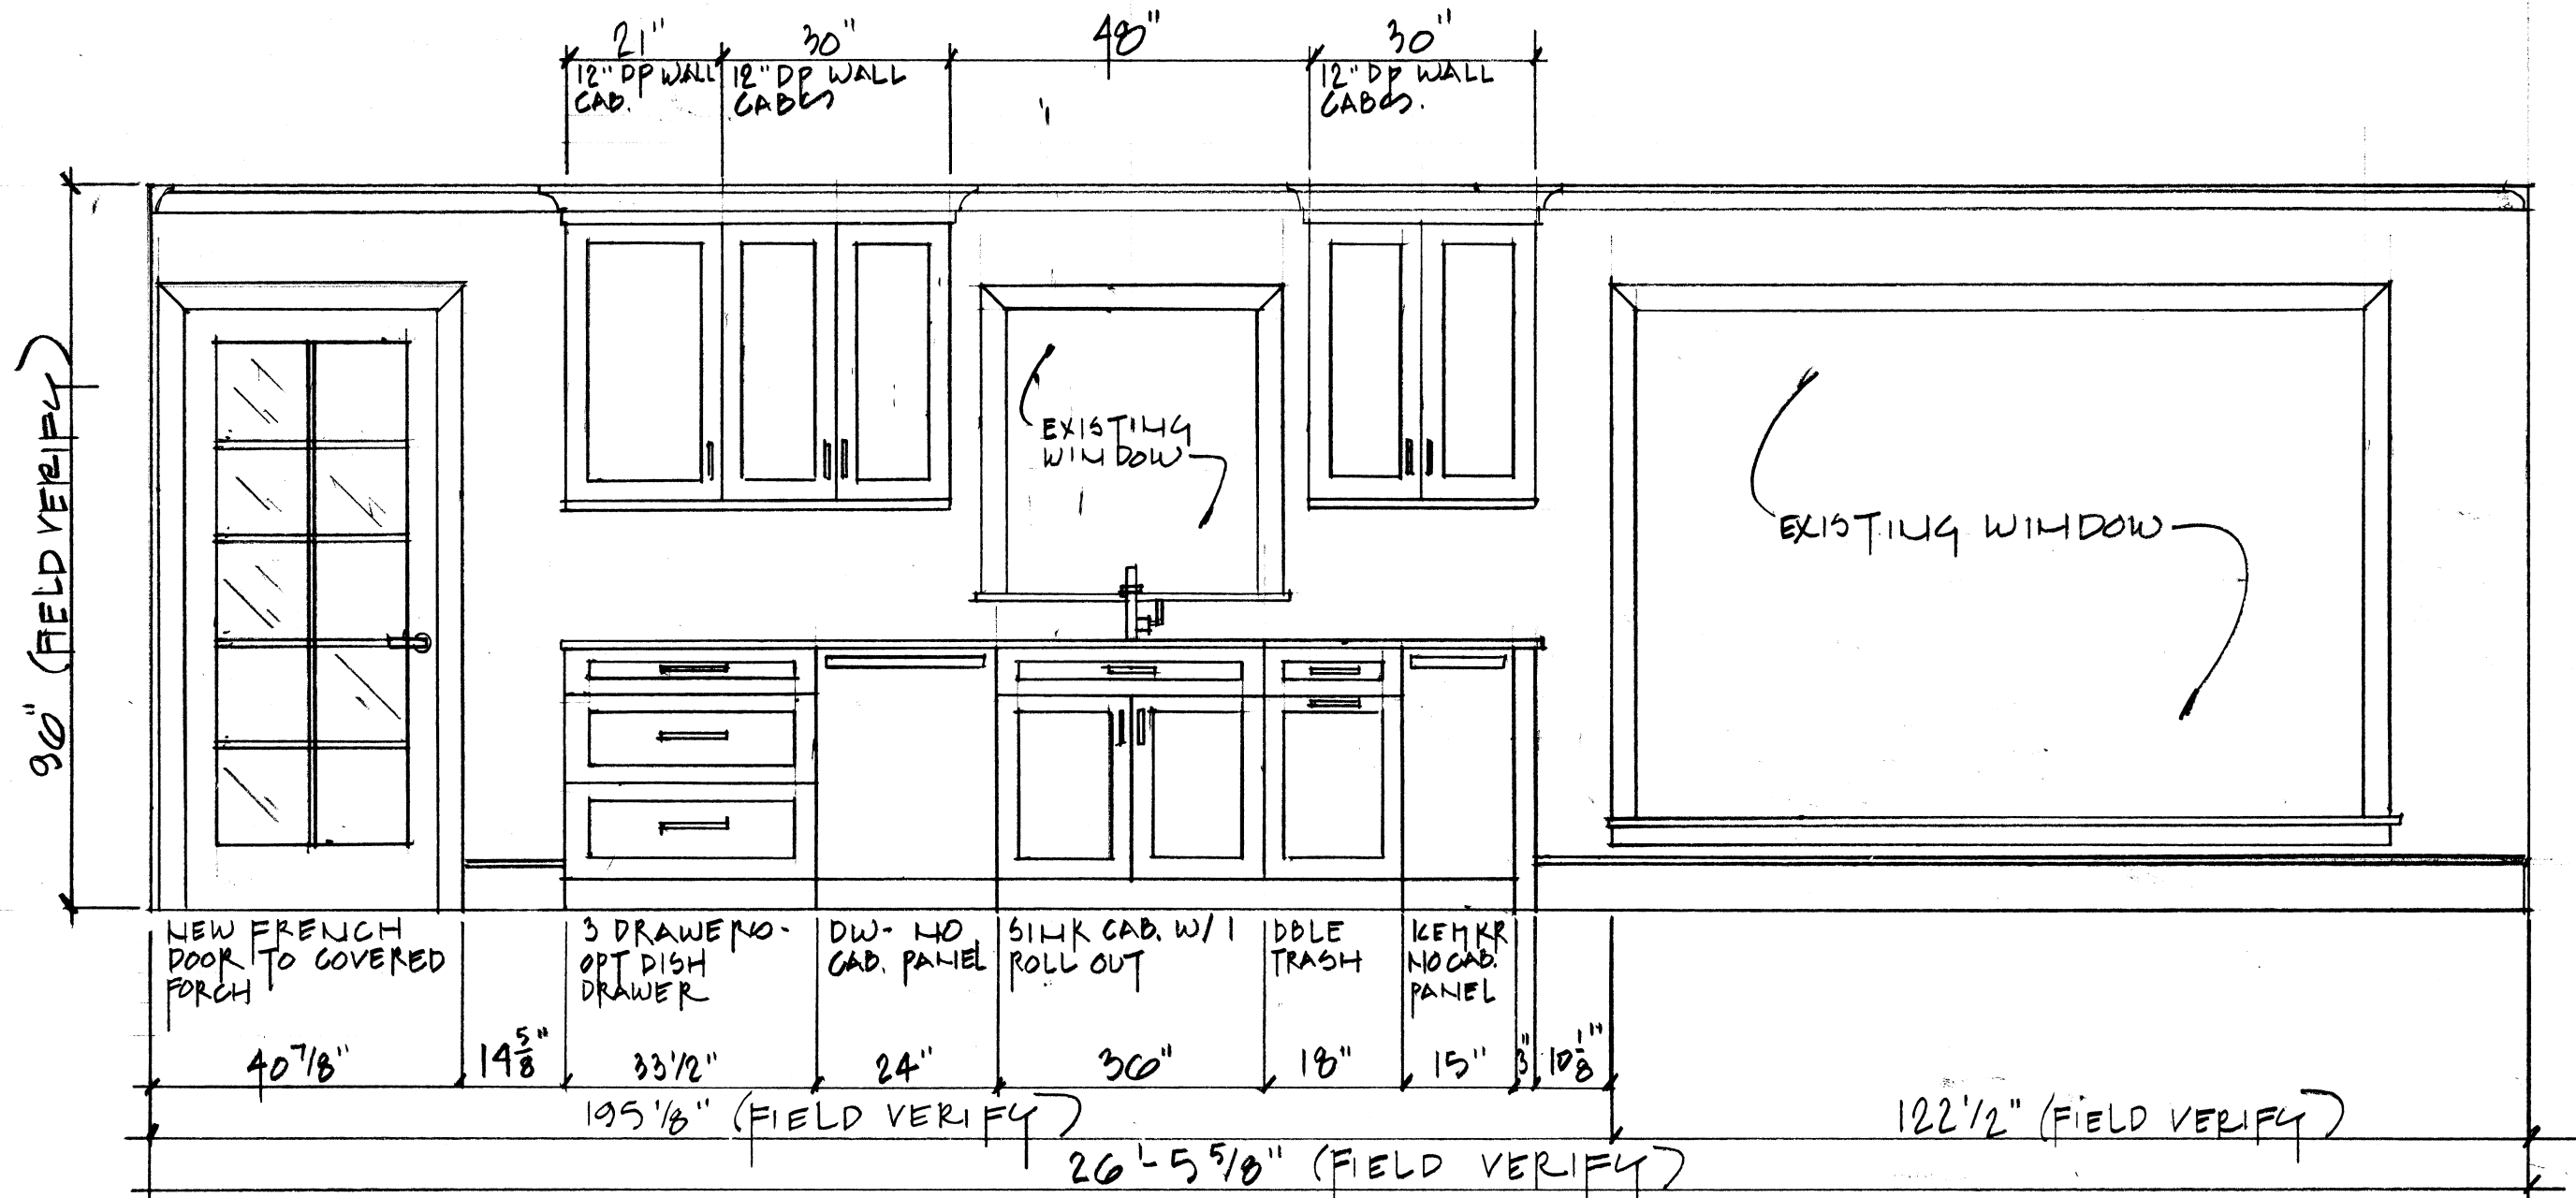

MARTINI: KITCHEN SINK WALL

TLHD, INC

NOTES: 1) PANELED ENDS TYPICAL ON ALL EXPOSED SIDES.
2) VERIFY CABINET PANELS ON APPLIANCES W/OWNER.

1/2" = 1'-0"

1.20.20

